



열사용시설 기계실 P & ID (급탕 일반열교환방식)

(제3조 제3항 및 제6조 관련) <개정 00.1.1, 06.1.1, 06.5.15, 09.9.1, 12.11.5, 17.11.24, 18.10.31>

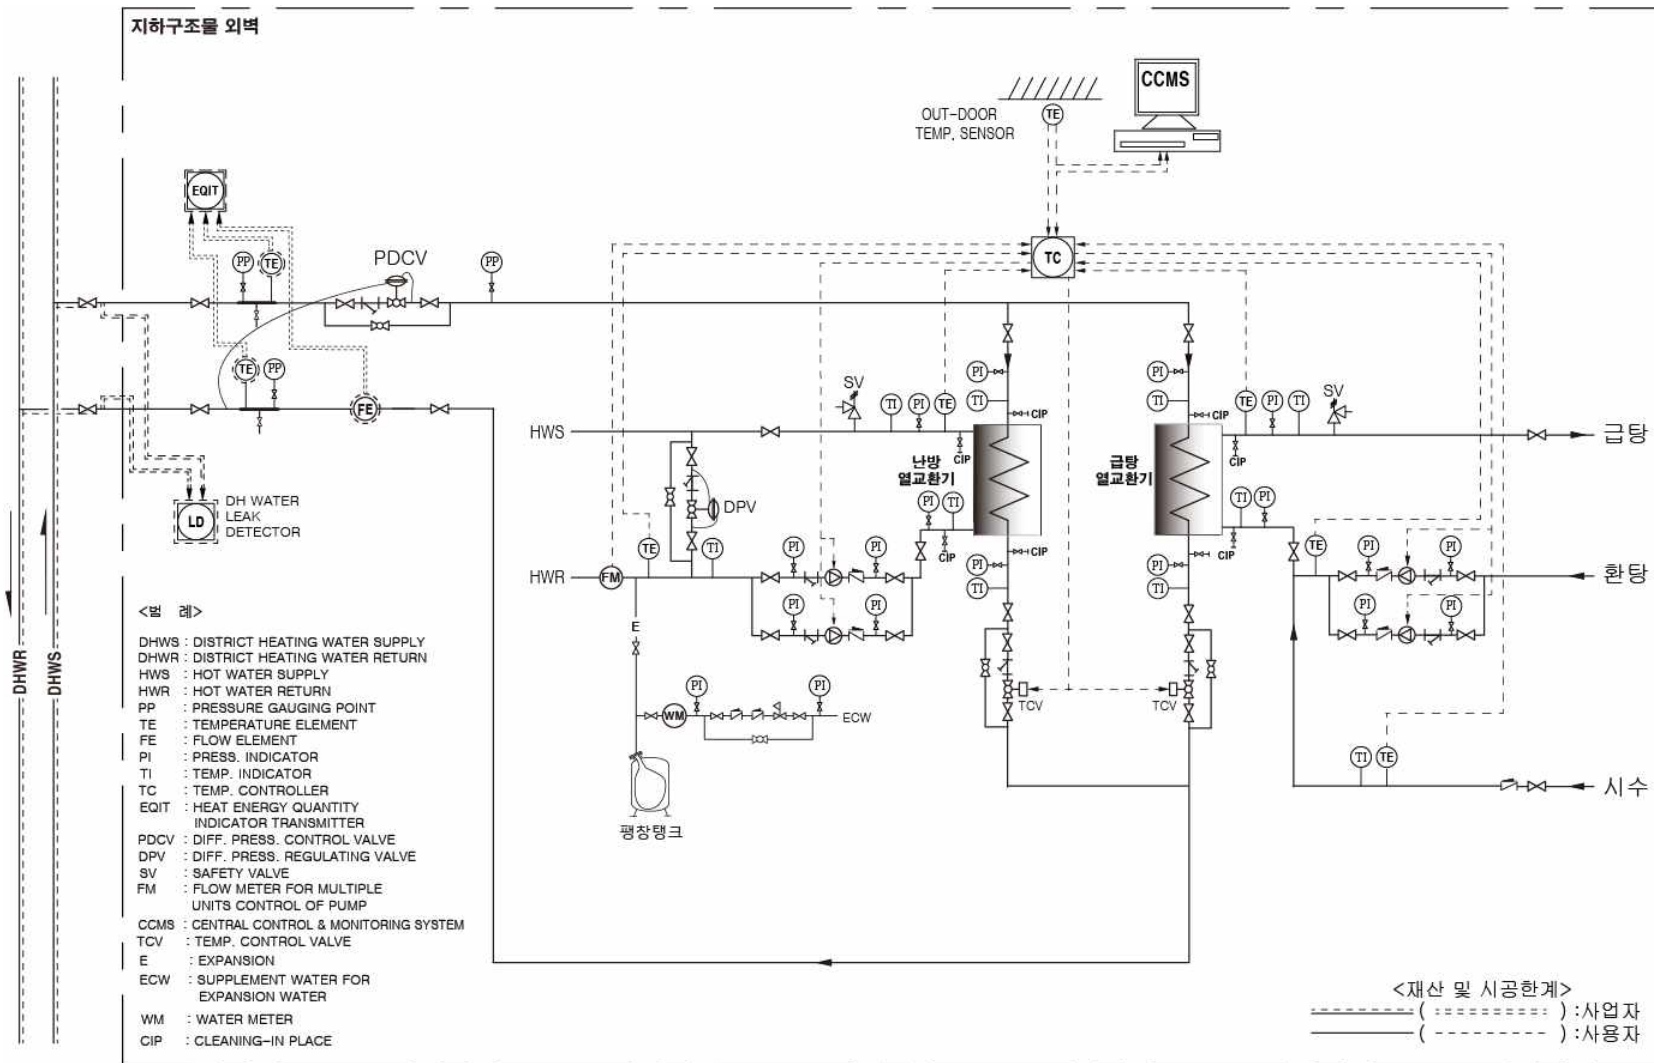

(제3조 제3항 및 제6조 관련) <신설 00.1.1, 개정 06.1.1, 06.5.15, 09.9.1, 12.11.5, 17.11.24, 18.10.31>

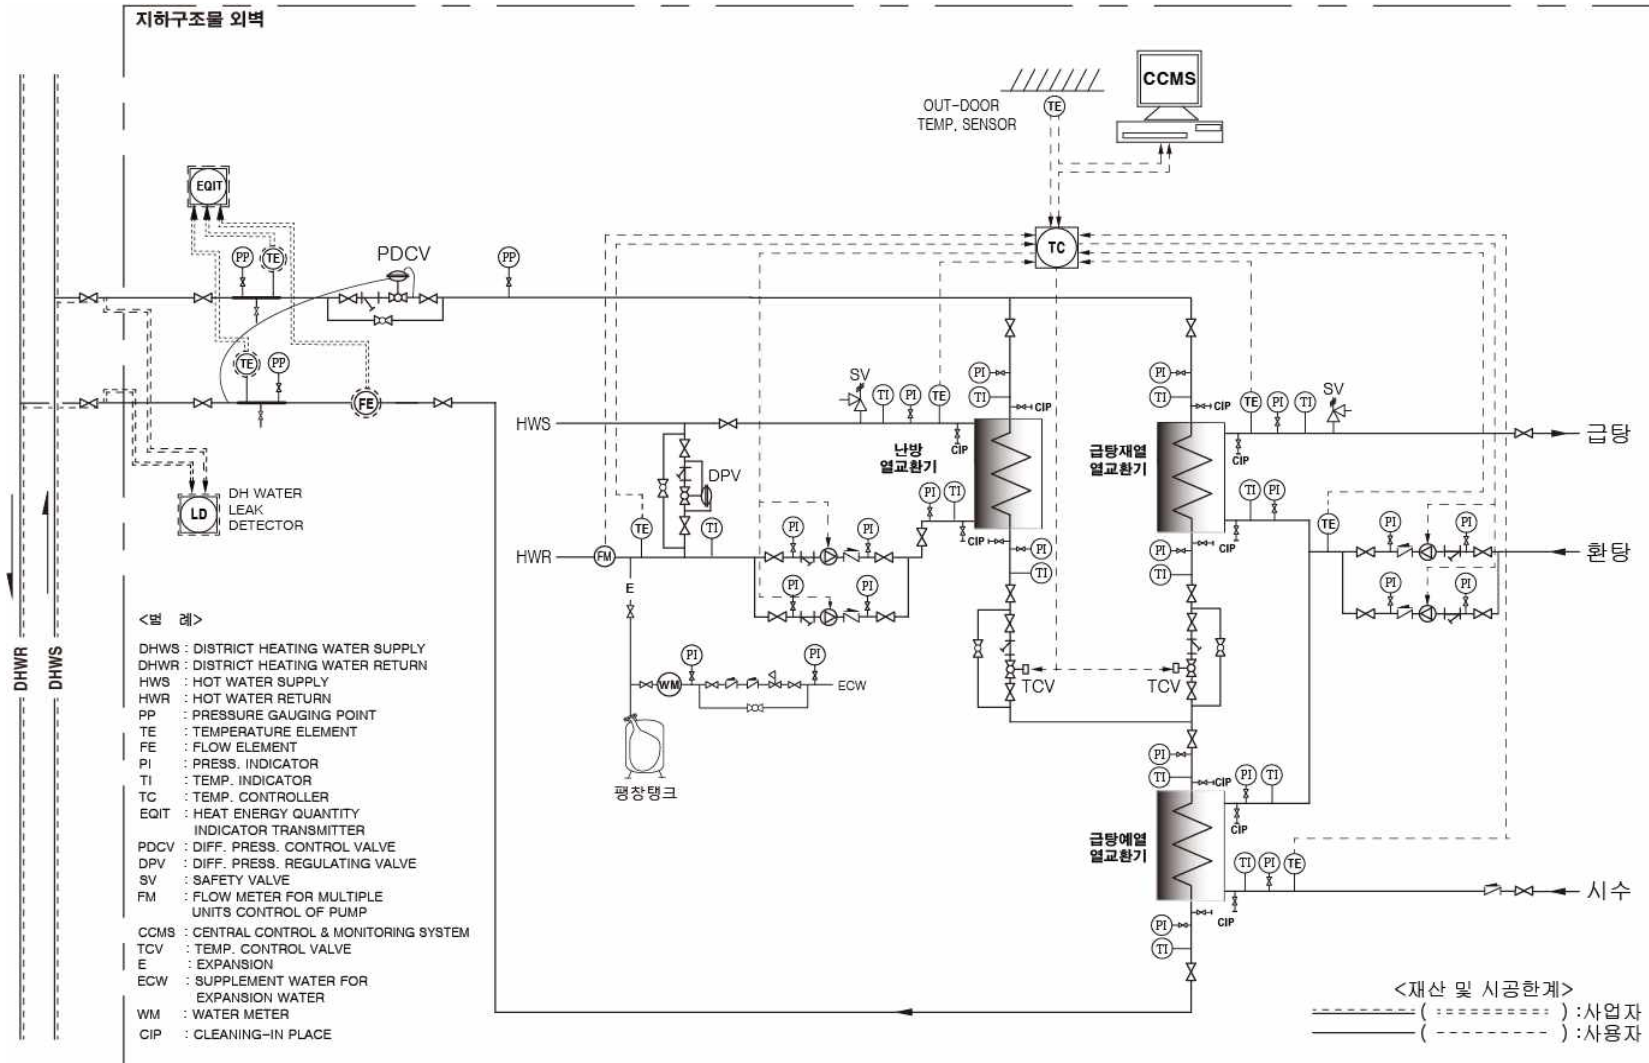

열사용시설 기계실 P & ID (냉난방건물, 급탕 2단열교환방식)

(제3조 제3항 및 제6조 관련) <개정 00.1.1, 06.1.1, 06.5.15, 09.9.1, 12.11.5, 17.11.24, 18.10.31, 22.10.04 >

