


【별표 4-1】

2차측배관 설계압력손실 선도(강관)


(제12조 제3항 관련) <개정 17.11.24>

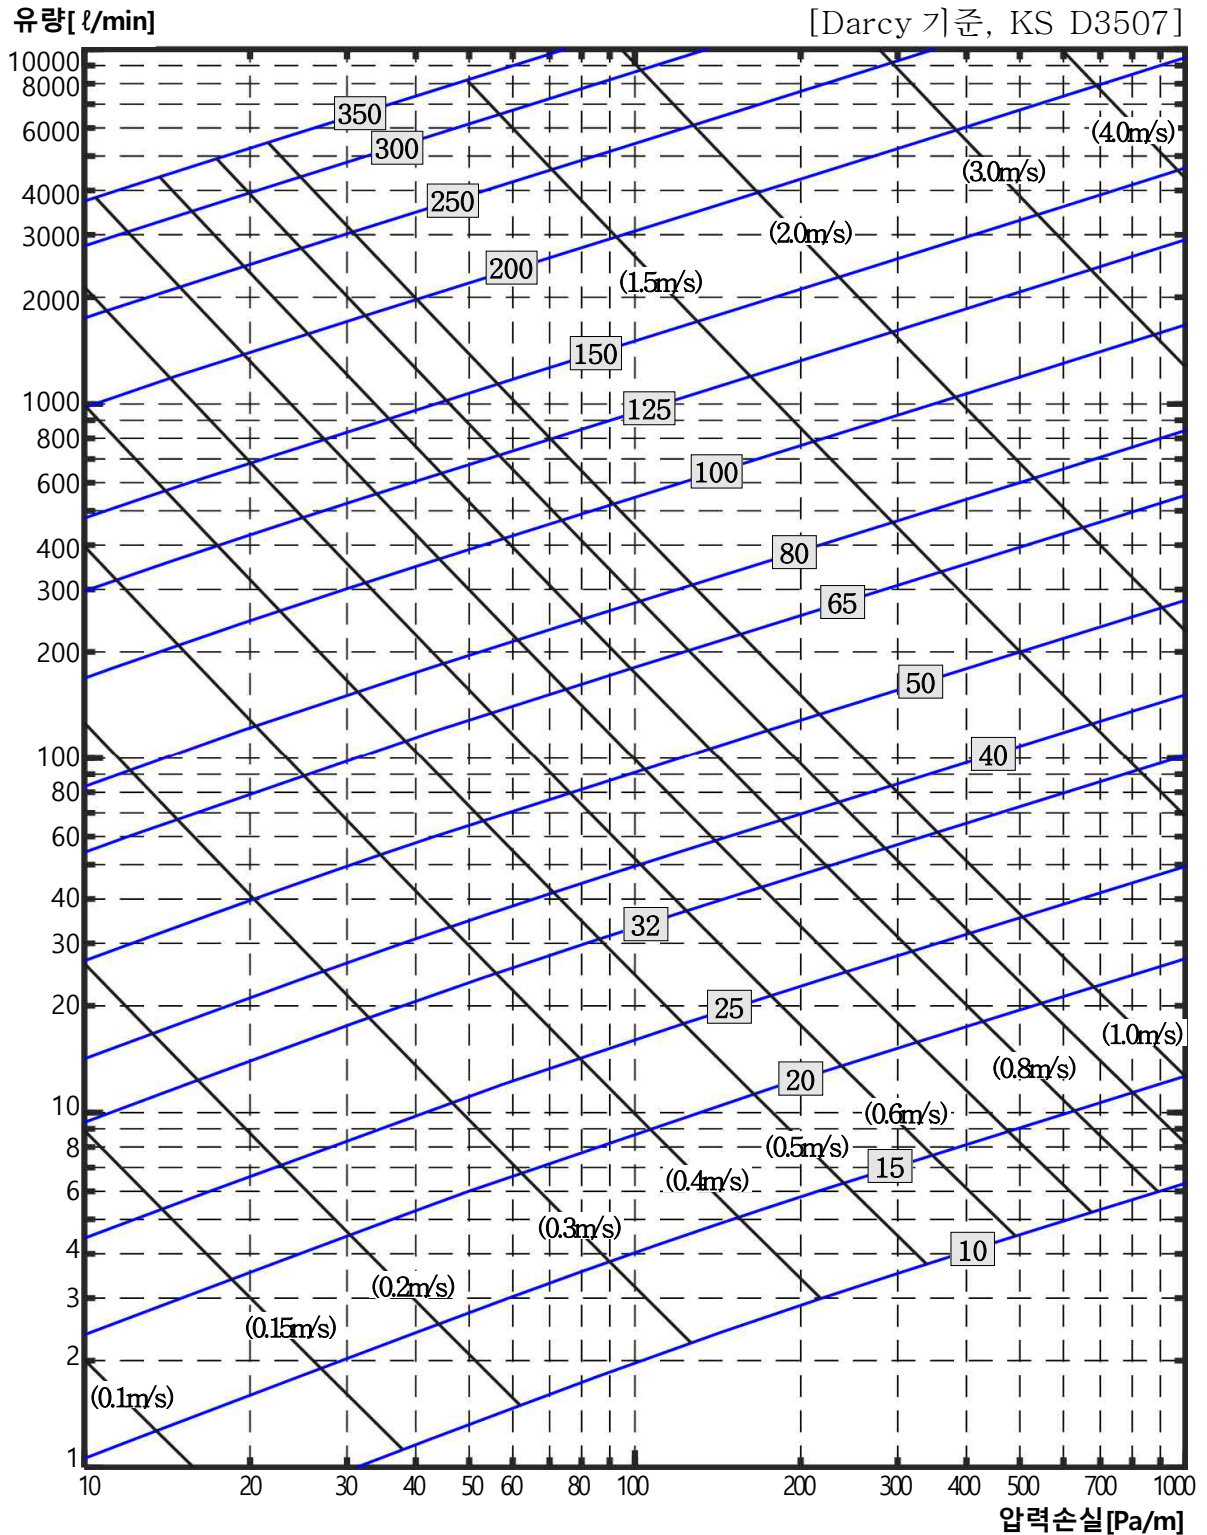

【별표 4-2】

2차측배관 설계압력손실 선도(스테인레스관)

(제12조 제3항 관련) <개정 17.11.24>

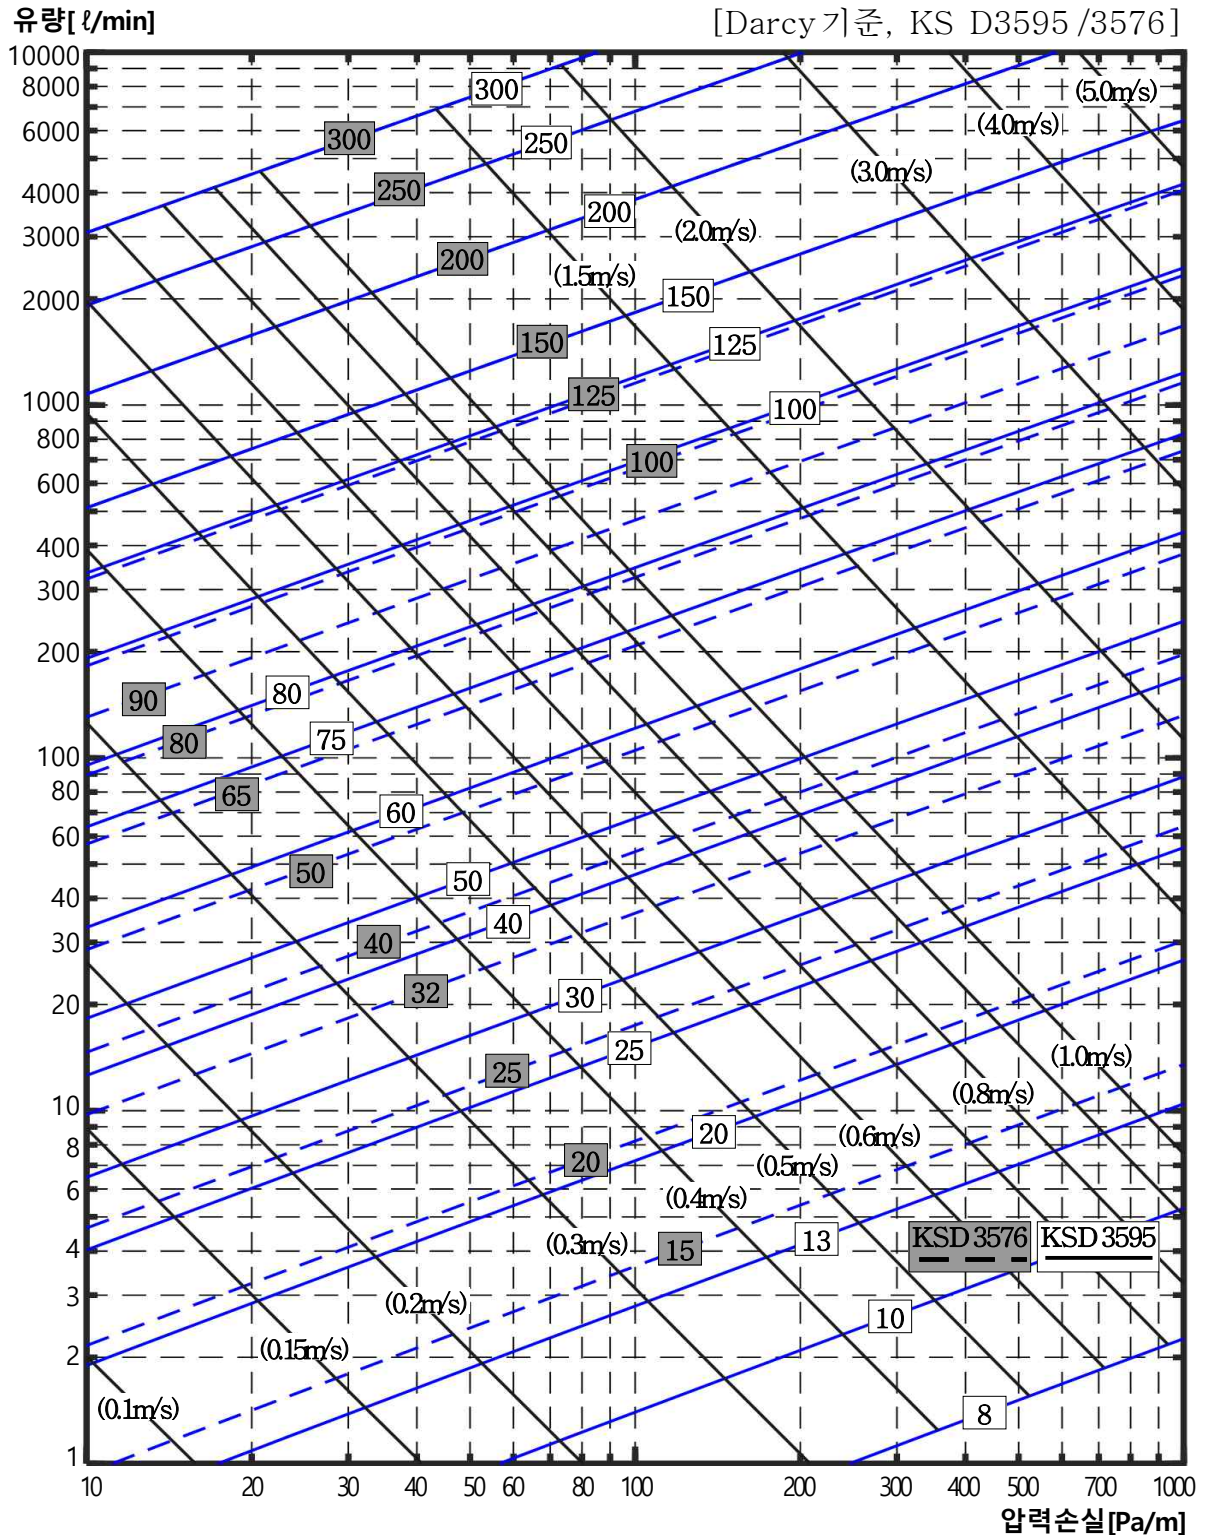

【별표 4-3】

2차측배관 설계압력손실 선도(동관)

(제12조 제3항 관련) <개정 17.11.24>

